


FIBERLIGHT, LLC
9101 FREEDOM CENTER BLVD
CONSTRUCTION DRAWING
MANASSAS, VIRGINIA (PRINCE WILLIAM COUNTY)

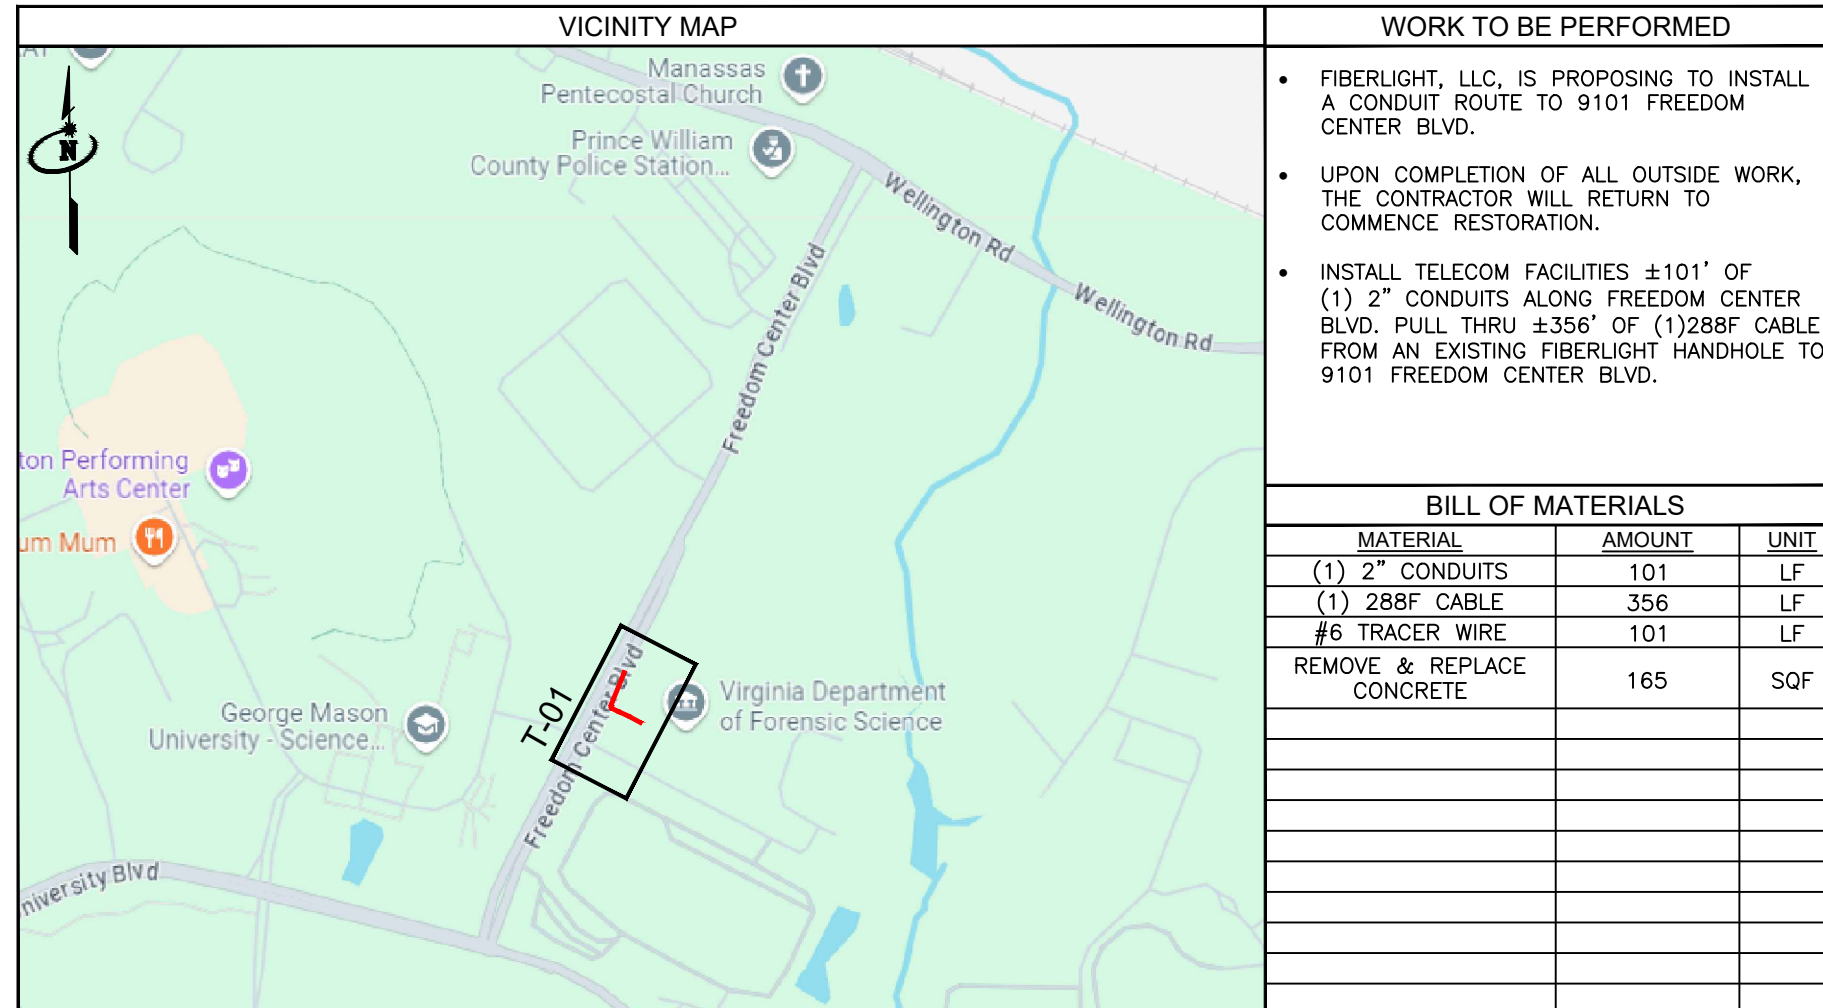

VA811.COM 1-800-552-7001	DISCLOSURE	ENGINEERING AND CONSTRUCTION FIRM	CLIENT/APPLICANT	REVISIONS				PROJECT INFORMATION			
	THIS DRAWING IS ONLY A GUIDELINE AND AS SUCH DOES NOT COVER EVERY POSSIBLE CONTINGENCY THAT MAY OCCUR.	 8093 Elm Drive Mechanicsville, Virginia 23111 PHONE: 804-321-8900 FAX: 804-442-2146	 45472 HOLIDAY DRIVE, SUITE 10 STERLING, VIRGINIA 20166 PHONE: 678-366-0027 FAX: 571-323-7655	REV	DATE	DESCRIPTION	BY	FISHEL PROJECT NUMBER: 052410328	DRAWN BY: CDL	CHECKED BY: JMH	
				01	09/26/24	TIE-IN UPDATE	JMH	DRAWING TITLE: 9101 FREEDOM CENTER BLVD	DRAWING TYPE: CONSTRUCTION		
				02	10/18/24	APPROVED PERMIT	JMH	DATE: 12/24/2024	SCALE:		
				03	12/24/24	INSTALLATION METHOD UPDATE	JMH	PAGE INFORMATION			
								COVER	T-00		
										SHEET 1 OF 7	

SYMBOLS

CLIENT CONTACTS:

FIBERLIGHT, LLC
EVAN MOSHONISIOTIS (443)–807–1340
JEFFREY ANDERSON (240)–674–3952

FISHEL CONTACTS:

ENGINEERING:
GERSON HERRERA (804)–382–6259
JAZMIN HARRIS (540)–395–5430

CONSTRUCTION:
DANNY KRAUS (703)–335–5301

UTILITIES:

MISS UTILITY (VA) 1–800–552–7001

PERMITTING AGENCIES:

VDOT–PRINCE WILLIAM COUNTY 1–703–366–1916
MANASSAS PERMITTING 1–703–257–8278

LINETYPES:

	B/C	BACK OF CURB		P/L	PROPERTY LINE
	B/E	BUILDING EDGE			PROPOSED TELECOM RUNNING LINE
	CATV	CABLE TV			PROPOSED PULL THROUGH
	C/L	CENTERLINE			RAILROAD
	DITCH	DITCH LINE		R/W	RIGHT–OF–WAY
	TOP BANK	TOP OF BANK		SAN	SANITARY SEWER LINE
	E/P	EDGE OF PAVEMENT			SILT FENCE
	UGE	ELECTRIC		STM	STORM LINE
	X	FENCE		UGT	TELEPHONE LINE
	E/G	EDGE OF GRAVEL		TR	TRAFFIC SIGNAL LINE
	F/C	FRONT OF CURB		W	WATER LINE
	G	GAS LINE			WALL
		GUARDRAIL			WOODS/LANDSCAPING
	LOD	LIMITS OF DISTURBANCE			

ELECTRIC

	ELECTRIC MANHOLE
	ELECTRIC HANDHOLE
	ELECTRIC TRANSFORMER
	POWER POLE
	GUY WIRE
	PARKING METER
	STREET LIGHT
	TRAFFIC CONTROL BOX
	TRAFFIC POLE
	TRAFFIC SIGNAL

GAS

	GAS MANHOLE
	GAS VALVE
	GAS MARKER TUBE

SEWER/STORM

	SEWER MANHOLE
	SEWER CLEANOUT
	STORM DRAIN MANHOLE
	GRATE INLET
	CATCH BASIN
	DROP INLET

WATER

	WATER MANHOLE
	WATER VALVE
	WATER METER
	FIRE HYDRANT
	IRRIGATION VALVE
	WELL
	WATER MARKER TUBE

TELEPHONE/TELECOM

	PROPOSED TELECOM HANDHOLE
	PROPOSED TELECOM VAULT
	PROPOSED TELECOM MANHOLE
	TELECOM MANHOLE
	TELECOM VAULT/HANDHOLE
	TELEPHONE PEDESTAL
	FIBER MARKER TUBE
	TELECOM CABINET

GENERAL

	SIGN
	BORE PIT
	TREE
	MAILBOX
	PROPERTY CORNER

MISC.

	LANDSCAPED AREA
	RETENTION POND
	WETLANDS

VA811.COM 1-800-552-7001

DISCLOSURE

THIS DRAWING IS ONLY A GUIDELINE AND AS SUCH DOES NOT COVER EVERY POSSIBLE CONTINGENCY THAT MAY OCCUR.

INFORMATION ON THESE SHEETS HAVE BEEN PREPARED FROM THE BEST AVAILABLE INFORMATION AND SOURCES. UTILITY LOCATIONS, SIZES, AND DEPTHS ARE APPROXIMATE (UNLESS OTHERWISE NOTED) AND HAVE NOT BEEN EXCAVATED TO DETERMINE EXACT LOCATION . UTILITY/FACILITY LOCATIONS ARE BASED ON RECORDS/VERBAL INFORMATION AND PHYSICAL FEATURES AT THE TIME OF THE SURVEY.

INFORMATION ON THIS DOCUMENT IS PROPRIETARY AND SHALL NOT BE USED, COPIED, REPRODUCED, OR DISCLOSED IN WHOLE OR IN PART WITHOUT WRITTEN CONSENT.

ENGINEERING AND CONSTRUCTION FIRM



8093 Elm Drive Mechanicsville, Virginia 23111
PHONE: 804–321–8900 FAX: 804–442–2146

CLIENT/APPLICANT



45472 HOLIDAY DRIVE, SUITE 10 STERLING, VIRGINIA 20166
PHONE: 678–366–0027 FAX: 571–323–7655

REVISIONS

REV	DATE	DESCRIPTION	BY
01	09/26/24	TIE–IN UPDATE	JMH
02	10/18/24	APPROVED PERMIT	JMH
03	12/24/24	INSTALLATION METHOD UPDATE	JMH

PROJECT INFORMATION

FISHEL PROJECT NUMBER: 052410328	DRAWN BY: CDL	CHECKED BY: JMH
DRAWING TITLE: 9101 FREEDOM CENTER BLVD		DRAWING TYPE: CONSTRUCTION
DATE: 12/24/2024		SCALE:

PAGE INFORMATION

LEGEND

T–00A

SHEET 2 OF 7



GENERAL NOTES:

- 1. ALL WORK WILL COMPLY WITH APPLICABLE LOCAL, STATE, AND FEDERAL REGULATORY AGENCIES, INCLUDING, BUT NOT LIMITED TO, OSHA, NESC, DOT, RPA, ETC. GENERAL NOTES WILL APPLY TO ALL DRAWINGS.
- 2. THE CONTRACTOR WILL NOTIFY (IF APPLICABLE) THE ADJACENT PROPERTY OWNERS A MINIMUM OF 24 HOURS IN ADVANCE OF CONSTRUCTION.
- 3. ALL TRAFFIC CONTROL DEVICES WILL BE IN PLACE PRIOR TO CONSTRUCTION. DEVICES NO LONGER NEEDED WILL BE REMOVED AS QUICKLY AS POSSIBLE.
- 4. PEDESTRIAN TRAFFIC AREAS MUST BE MAINTAINED AT ALL TIMES. PEDESTRIANS WILL NOT BE ROUTED ON TO PRIVATE PROPERTY.
- 5. NO MATERIALS OR EQUIPMENT WILL BE STORED OR ALLOWED TO STAND UNPROTECTED WHERE PEDESTRIAN OR VEHICULAR TRAFFIC IS PRESENT.
- 6. NO EQUIPMENT OR MATERIALS WILL BE STORED ON ROAD SURFACE DURING NON–WORK PERIODS.
- 7. NO EQUIPMENT OR MATERIALS MAY BE STORED ON THE SIDEWALK.
- 8. EXCAVATION MATERIAL WILL BE STORED AWAY FORM THE PAVED ROADWAY. ALL SPILLED MATERIAL WILL BE PICKED UP IMMEDIATELY.
- 9. MUNICIPAL ROAD SIGNS, DELINEATORS, GUARDRAILS, ETC. WILL NOT BE REMOVED WITHOUT PRIOR WRITTEN PERMISSION FROM THE APPROVING AUTHORITY.
- 10. ALL WORK WILL BE PERFORMED IN ACCORDANCE WITH THE CITY, COUNTY, AND STATE SPECIFICATIONS AND STANDARDS.

CONSTRUCTION PERIOD:

CONSTRUCTION IN THE RIGHT OF WAY ARE TO BE DETERMINED. REFERENCE CONSTRUCTION SCHEDULE FOR TIMELINE OF SPECIFIC PROJECT.

EROSION SEDIMENTATION CONTROL PROGRAM:

EROSION AND SEDIMENTATION CONTROLS SHOWN ARE PROVIDED TO ACCOMMODATE ONSITE DRAINAGE AREAS DURING THE CONSTRUCTION PHASE. ADDITIONAL OR REVISED CONTROLS MAY BE INSTALLED AS DETERMINED NECESSARY. EROSION AND SEDIMENTATION CONTROL MEASURES SHALL BE CONSTRUCTED AND MAINTAINED ACCORDING TO STANDARDS AND SPECIFICATIONS IN THE CURRENT VIRGINIA EROSION AND SEDIMENT CONTROL HANDBOOK.

PHASE OF LAND DISTURBING ACTIVITY:

CONTROLS SHOWN SHALL BE INSTALLED AS THE FIRST ITEM OF CONSTRUCTION AND MAINTAINED FOR CONSTRUCTION ACTIVITIES LASTING MORE THAN A ONE DAY SCHEDULE. ALL AREAS NOT TO BE IMMEDIATELY BUILT UPON SHALL BE SEEDED FOR TEMPORARY VEGETATION. ALL CONTROLS ARE TO REMAIN IN PLACE FOR THE DURATION OF THE JOB. REMOVAL, REGRADING AND SEEDING OF THE TEMPORARY DIVERSION DIKES WILL BE THE FINAL ACT OF GRADING IF REQUIRED.

SEQUENCE OF CONSTRUCTION:

- 1. PLACEMENT OF EROSION AND SEDIMENTATION CONTROLS
- 2. TRENCHING AND/OR DIRECTIONAL BORING
- 3. UTILITY INSTALLATION
- 4. FINAL GRADING AND VEGETATION
- 5. REMOVAL OF CONTROLS


GENERAL LAND CONSERVATION NOTES:

- 1. NO DISTURBED AREA WILL BE DENUDED FOR MORE THAN SEVEN (7) CALENDAR DAYS UNLESS AUTHORIZED BY PRINCE WILLIAM COUNTY, VIRGINIA.
- 2. ALL EROSION AND SEDIMENTATION CONTROL MEASURES SHALL BE PLACED AS THE FIRST STEP IN GRADING.
- 3. ELECTRIC POWER, TELEPHONE AND GAS SUPPLY TRENCHES SHALL BE COMPACTED, SEEDED AND MULCHED WITHIN FIVE (5) DAYS OF BACKFILL, SHOULD EXCAVATION OCCUR.
- 4. ALL TEMPORARY EARTH BERMS, DIVERSION DIKES, SILT DAMS, AND SOIL STOCKPILES SHALL BE SEEDED AND MULCHED FOR TEMPORARY VEGETATIVE COVER IMMEDIATELY AFTER GRADING. STRAW OR HAY IS REQUIRED.
- 5. DURING CONSTRUCTION, ALL STORM SEWER INLETS SHALL BE PROTECTED BY SILT TRAPS MAINTAINED AND MODIFIED AS REQUIRED CONSTRUCTION PROGRESS.
- 6. ANY DISTURBED AREA NOT COVERED BY NOTE 1 ABOVE AND NOT PAVED, SODDED, OR BUILT UPON BY NOVEMBER 1, OR DISTURBED AFTER THAT DATE SHALL BE MULCHED WITH HAY OR STRAW MULCH AT THE RATE OF TWO (2) TONS PER ACRE.
- 7. AT THE COMPLETION OF CONSTRUCTION PROJECT AND PRIOR TO RELEASE OF THE BOND, ALL TEMPORARY SILTATION AND EROSION CONTROLS SHALL BE REMOVED UPON THE APPROVAL OF PRINCE WILLIAM COUNTY, AND ALL DENUDED AREAS SHALL BE STABILIZED WITH VEGETATION.
- 8. ALL EROSION AND SEDIMENTATION CONTROL MEASURES SHALL MEET THE STANDARDS AND SPECIFICATIONS OF THE CURRENT VIRGINIA EROSION AND SEDIMENT CONTROL HANDBOOK.
- 9. NO MORE THAN 500 LINEAR FEET OF TRENCH MAY BE OPENED AT ONE TIME PER CREW.
- 10. EXCAVATION MATERIAL SHALL BE PLACED ON THE UPHILL SIDE OF THE TRENCH.
- 11. EFFLUENT FROM THE DEWATERING OPERATIONS SHALL BE FILTERED OR PASSED THROUGH AND APPROVED SEDIMENT TRAPPING DEVICE, OR BOTH, AND DISCHARGED IN A MANNER THAT DOES NOT ADVERSELY AFFECT FLOWING STREAMS OR OFF–SITE PROPERTY.
- 12. MATERIAL USED FOR BACKFILLING TRENCHES SHALL BE PROPERLY COMPACTED IN ORDER TO MINIMIZE EROSION AND PROMOTE STABILIZATION.
- 13. RESTABILIZATION SHALL BE ACCOMPLISHED IN ACCORDANCE WITH THESE REGULATIONS.
- 14. APPLICABLE SAFETY REGULATIONS SHALL BE COMPLIED WITH.
- 15. WHERE CONSTRUCTION VEHICLE ACCESS ROUTES INTERSECT PAVED OR PUBLIC ROADS, PROVISIONS SHALL BE MADE TO MINIMIZE THE TRANSPORT OF SEDIMENT IS TRANSPORTED ONTO A PAVED OR PUBLIC ROAD SURFACE, THE ROAD SURFACE SHALL BE CLEANED THOROUGHLY AT THE END OF EACH DAY. SEDIMENT SHALL BE REMOVED FROM THE ROADS BY SHOVELING OR SWEEPING AND TRANSPORTED TO A SEDIMENT CONTROL DISPOSAL AREA. STREET WASHING SHALL BE ALLOWED ONLY AFTER SEDIMENT IS REMOVED IN THIS MANNER.

CONSTRUCTION NOTES:

- 1. FIBER OPTIC WARNING TAPE WILL BE PLACED 18 INCHES ABOVE TOP OF CONDUITS IN ALL EXCAVATIONS.
- 2. VERIFICATION OF LOCATION OF EXISTING UTILITY CROSSINGS IS THE RESPONSIBILITY OF THE CONTRACTOR. HAND DIGGING WILL BE UTILIZED WHERE REQUIRED.
- 3. CALL THE LOCAL UTILITY AT LEAST 72 HOURS IN ADVANCE OF ANY CONSTRUCTION.
- 4. SEPARATION BETWEEN PROPOSED CONDUIT AND OTHER UTILITIES WILL BE MAINTAINED PER THE STANDARD OF EACH UTILITY TYPE.
- 5. CONDUIT CAPS WILL BE PLACED ON THE ENDS OF ALL VACANT DUCTS DURING CONSTRUCTION, UPON COMPLETION, AND WHILE AWAITING FIBER INSTALLATION.
- 6. ALL INSTALLED DUCTS WILL BE PROOFED USING A MANDRILL 1/4 INCH SMALLER THAN THE PIPE ID PVC.
- 7. THE MINIMUM BENDING RADIUS OF FIBER CABLE WILL BE 48 INCHES.
- 8. MAXIMUM CABLE INSTALLATION TENSION WILL NOT EXCEED 600 POUNDS. A 600 POUND BREAKAWAY SWIVEL WILL BE USED DURING PULLING.
- 9. THE REMOVAL AND STORAGE OF ALL SHRUBBERY TO BE REPLACED IS THE RESPONSIBILITY OF THE CONTRACTOR.
- 10. THE CONTRACTOR WILL RESTORE ALL DISTURBED AREAS TO THEIR ORIGINAL OR BETTER CONDITION.
- 11. IT IS THE RESPONSIBILITY OF THE CONTRACTOR TO MAINTAIN CONSTRUCTION AS–BUILT DRAWINGS AND PRESENT A COMPLETE SET OF RED–LINED DRAWINGS TO THE CUSTOMER ONCE THE WORK IS COMPLETE.
- 12. CONDUITS WILL BE TERMINATED AT THE BOTTOM OF MANHOLE/HANDHOLE.
- 13. PLACE 100 FEET FIBER SLACK COIL IN EACH MANHOLE/HANDHOLE.
- 14. PLACE FIBER MARKER AT EACH MANHOLE IN LINE OF SITE.
- 15. HAND DIG UNDER ANY BURIED UTILITY CABLES AS REQUIRED.
- 16. PLACE 6” BEDDING OF #57 STONE FOR DRAINAGE ON ALL HANDHOLES.

VA811.COM 1-800-552-7001		DISCLOSURE	ENGINEERING AND CONSTRUCTION FIRM	CLIENT/APPLICANT	REVISIONS				PROJECT INFORMATION			
		THIS DRAWING IS ONLY A GUIDELINE AND AS SUCH DOES NOT COVER EVERY POSSIBLE CONTINGENCY THAT MAY OCCUR. INFORMATION ON THESE SHEETS HAVE BEEN PREPARED FROM THE BEST AVAILABLE INFORMATION AND SOURCES. UTILITY LOCATIONS, SIZES, AND DEPTHS ARE APPROXIMATE (UNLESS OTHERWISE NOTED) AND HAVE NOT BEEN EXCAVATED TO DETERMINE EXACT LOCATION . UTILITY/FACILITY LOCATIONS ARE BASED ON RECORDS/VERBAL INFORMATION AND PHYSICAL FEATURES AT THE TIME OF THE SURVEY. INFORMATION ON THIS DOCUMENT IS PROPRIETARY AND SHALL NOT BE USED, COPIED, REPRODUCED, OR DISCLOSED IN WHOLE OR IN PART WITHOUT WRITTEN CONSENT.	 8093 Elm Drive Mechanicsville, Virginia 23111 PHONE: 804-321-8900 FAX: 804-442-2146	 45472 HOLIDAY DRIVE, SUITE 10 STERLING, VIRGINIA 20166 PHONE: 678-366-0027 FAX: 571-323-7655	REV	DATE	DESCRIPTION	BY	FISHEL PROJECT NUMBER: 052410328	DRAWN BY: CDL	CHECKED BY: JMH	
					01	09/26/24	TIE-IN UPDATE	JMH	DRAWING TITLE: 9101 FREEDOM CENTER BLVD	DRAWING TYPE: CONSTRUCTION		
					02	10/18/24	APPROVED PERMIT	JMH	DATE: 12/24/2024	SCALE:		
					03	12/24/24	INSTALLATION METHOD UPDATE	JMH	PAGE INFORMATION			
							</					

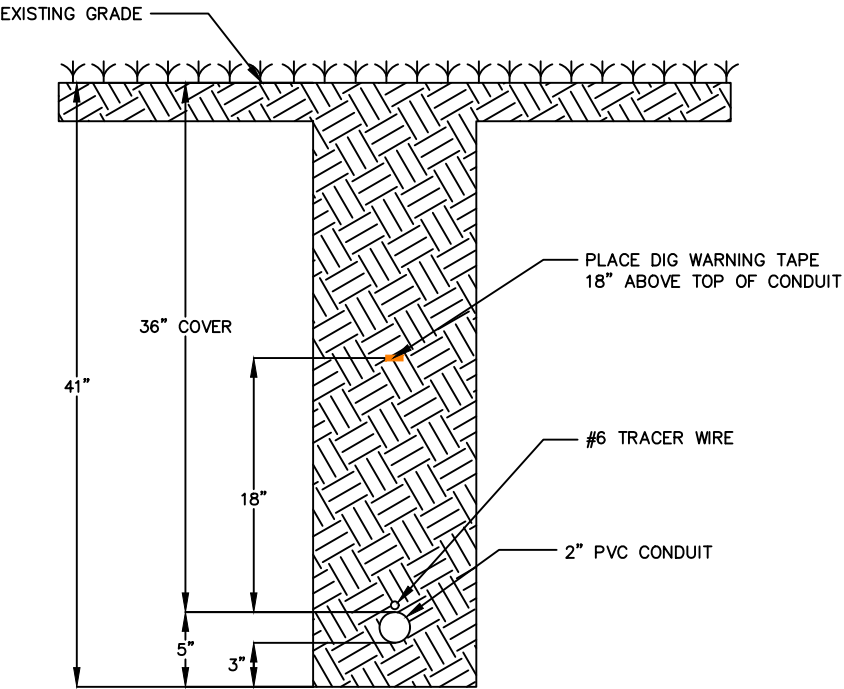

TYPICAL OPEN TRENCH DETAIL

- NOTES:
- 1) CONDUITS SHALL BE ONE (1)–2 PVC CONDUIT.
 - 2) DISTURBED AREA TO BE RESTORED TO EXISTING CONDITION.


VA811.COM 1-800-552-7001		DISCLOSURE	ENGINEERING AND CONSTRUCTION FIRM	CLIENT/APPLICANT	REVISIONS				PROJECT INFORMATION			
		THIS DRAWING IS ONLY A GUIDELINE AND AS SUCH DOES NOT COVER EVERY POSSIBLE CONTINGENCY THAT MAY OCCUR. INFORMATION ON THESE SHEETS HAVE BEEN PREPARED FROM THE BEST AVAILABLE INFORMATION AND SOURCES. UTILITY LOCATIONS, SIZES, AND DEPTHS ARE APPROXIMATE (UNLESS OTHERWISE NOTED) AND HAVE NOT BEEN EXCAVATED TO DETERMINE EXACT LOCATION . UTILITY/FACILITY LOCATIONS ARE BASED ON RECORDS/VERBAL INFORMATION AND PHYSICAL FEATURES AT THE TIME OF THE SURVEY. INFORMATION ON THIS DOCUMENT IS PROPRIETARY AND SHALL NOT BE USED, COPIED, REPRODUCED, OR DISCLOSED IN WHOLE OR IN PART WITHOUT WRITTEN CONSENT.	 8093 Elm Drive Mechanicsville, Virginia 23111 PHONE: 804-321-8900 FAX: 804-442-2146	 45472 HOLIDAY DRIVE, SUITE 10 STERLING, VIRGINIA 20166 PHONE: 678-366-0027 FAX: 571-323-7655	REV	DATE	DESCRIPTION	BY	FISHEL PROJECT NUMBER: 052410328	DRAWN BY: CDL	CHECKED BY: JMH	
					01	09/26/24	TIE-IN UPDATE	JMH	DRAWING TITLE: 9101 FREEDOM CENTER BLVD		DRAWING TYPE: CONSTRUCTION	
					02	10/18/24	APPROVED PERMIT	JMH	DATE: 12/24/2024		SCALE:	
					03	12/24/24	INSTALLATION METHOD UPDATE	JMH	PAGE INFORMATION			
					TYPICAL PAGE			T-00C				
SHEET 4 OF 7												

EXISTING UTILITY CROSSING TYPICALS


NOTES:

UTILITY DEPTH TO BE DETERMINED IN THE FIELD
LISTED SEPARATION TO BE MAINTAINED ABOVE OR BELOW CROSSING


ELECTRIC DETAIL
SCALE:NTS

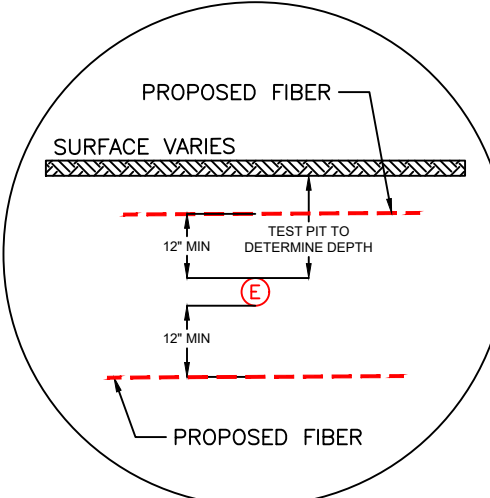


GAS DETAIL
SCALE:NTS

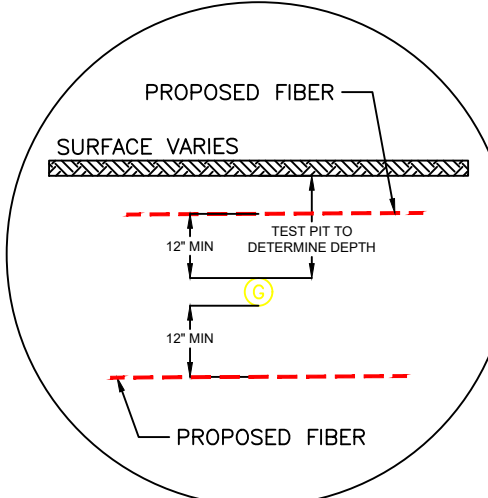


SEWER DETAIL
SCALE: NTS

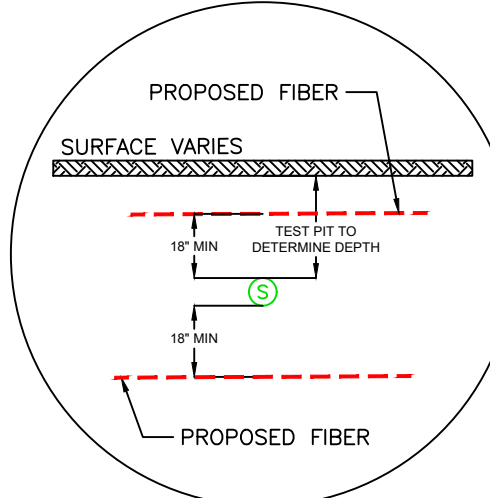


STORM DRAIN DETAIL
SCALE:NTS

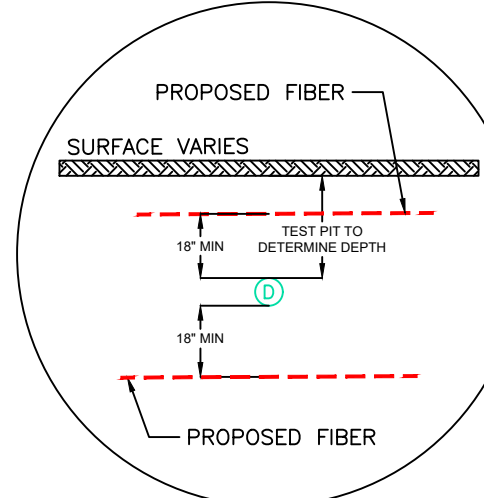


TELEPHONE DETAIL
SCALE:NTS

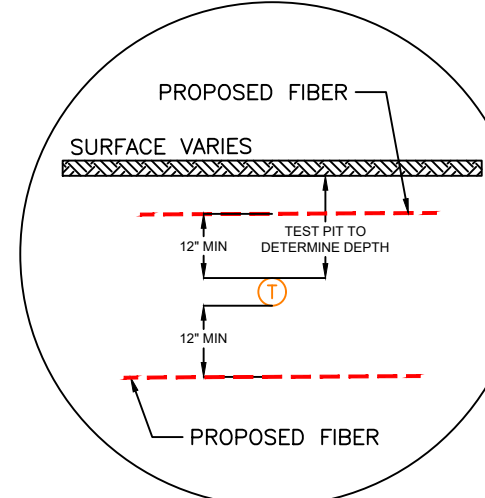


WATER DETAIL
SCALE:NTS

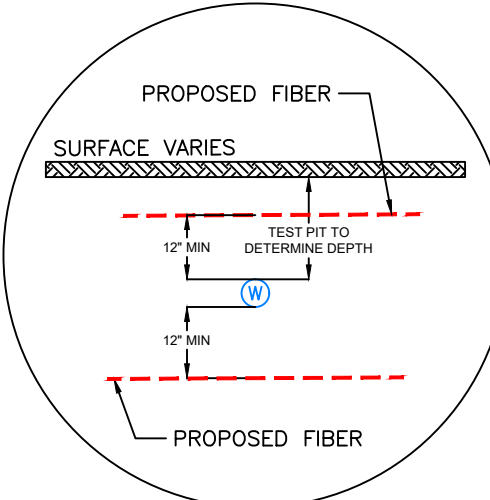


FIBER DETAIL
SCALE:NTS

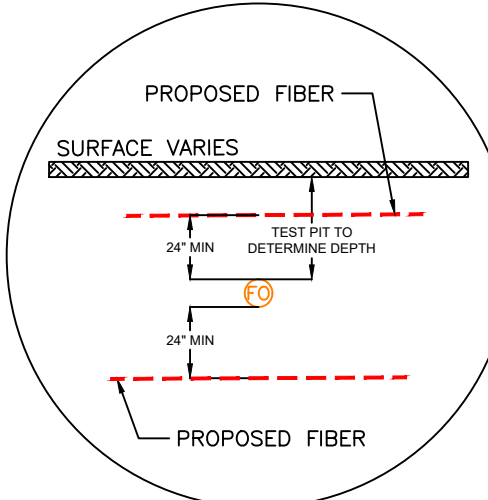


CULVERT DETAIL
SCALE:NTS

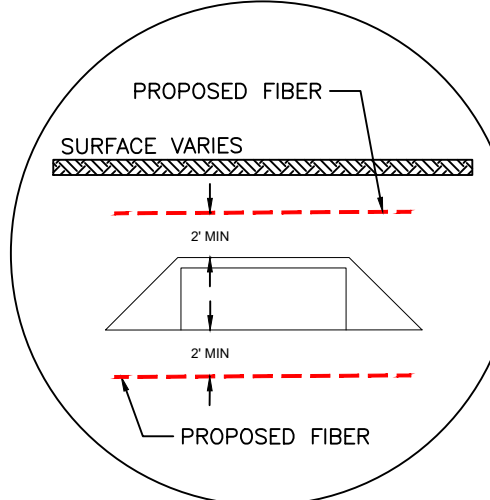

DRIVEWAY/PRIVATE RD
SCALE:NTS

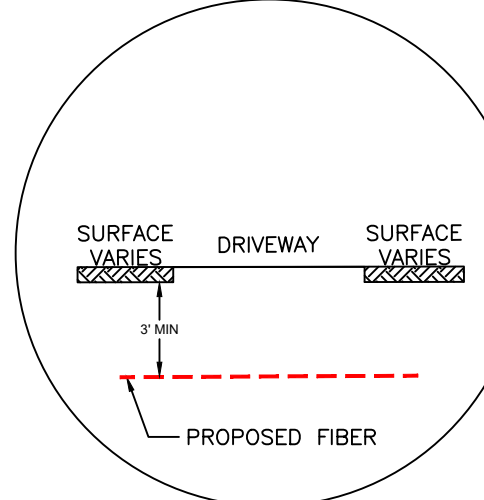

TRAFFIC SIGNAL DETAIL
SCALE:NTS

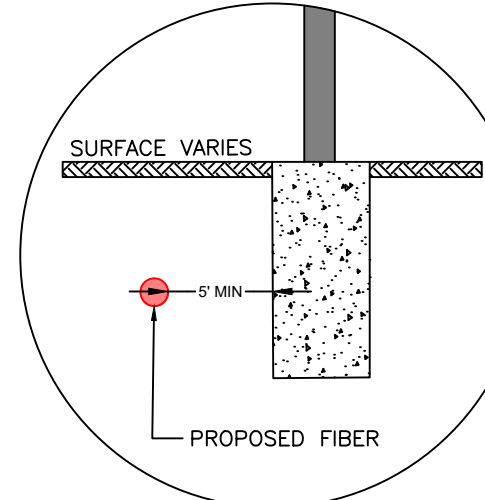

VA811.COM 1-800-552-7001

DISCLOSURE

THIS DRAWING IS ONLY A GUIDELINE AND AS SUCH DOES NOT COVER EVERY POSSIBLE CONTINGENCY THAT MAY OCCUR.

INFORMATION ON THESE SHEETS HAVE BEEN PREPARED FROM THE BEST AVAILABLE INFORMATION AND SOURCES. UTILITY LOCATIONS, SIZES, AND DEPTHS ARE APPROXIMATE (UNLESS OTHERWISE NOTED) AND HAVE NOT BEEN EXCAVATED TO DETERMINE EXACT LOCATION. UTILITY/FACILITY LOCATIONS ARE BASED ON RECORDS/VERBAL INFORMATION AND PHYSICAL FEATURES AT THE TIME OF THE SURVEY.

INFORMATION ON THIS DOCUMENT IS PROPRIETARY AND SHALL NOT BE USED, COPIED, REPRODUCED, OR DISCLOSED IN WHOLE OR IN PART WITHOUT WRITTEN CONSENT.

ENGINEERING AND CONSTRUCTION FIRM



8093 Elm Drive Mechanicsville, Virginia 23111
PHONE: 804-321-8900 FAX: 804-442-214

CLIENT/APPLICANT




45472 HOLIDAY DRIVE, SUITE 10 STERLING, VIRGINIA 2016
PHONE: 678-366-0027 FAX: 571-323-7655

REVISIONS


REV	DATE	DESCRIPTION	E
01	09/26/24	TIE-IN UPDATE	JL
02	10/18/24	APPROVED PERMIT	JL
03	12/24/24	INSTALLATION METHOD UPDATE	JL

PROJECT INFORMATION

FISHEL PROJECT NUMBER	052410328	DRAWN BY:	CDL	CHECKED BY:	JMH
DRAWING TITLE:	9101 FREEDOM CENTER BLVD			DRAWING TYPE:	CONSTRUCTION
DATE:	12/24/2024			SCALE:	
PAGE INFORMATION					
TYPICAL CROSSINGS				T-00E	
				SHEET 5 OF 3	

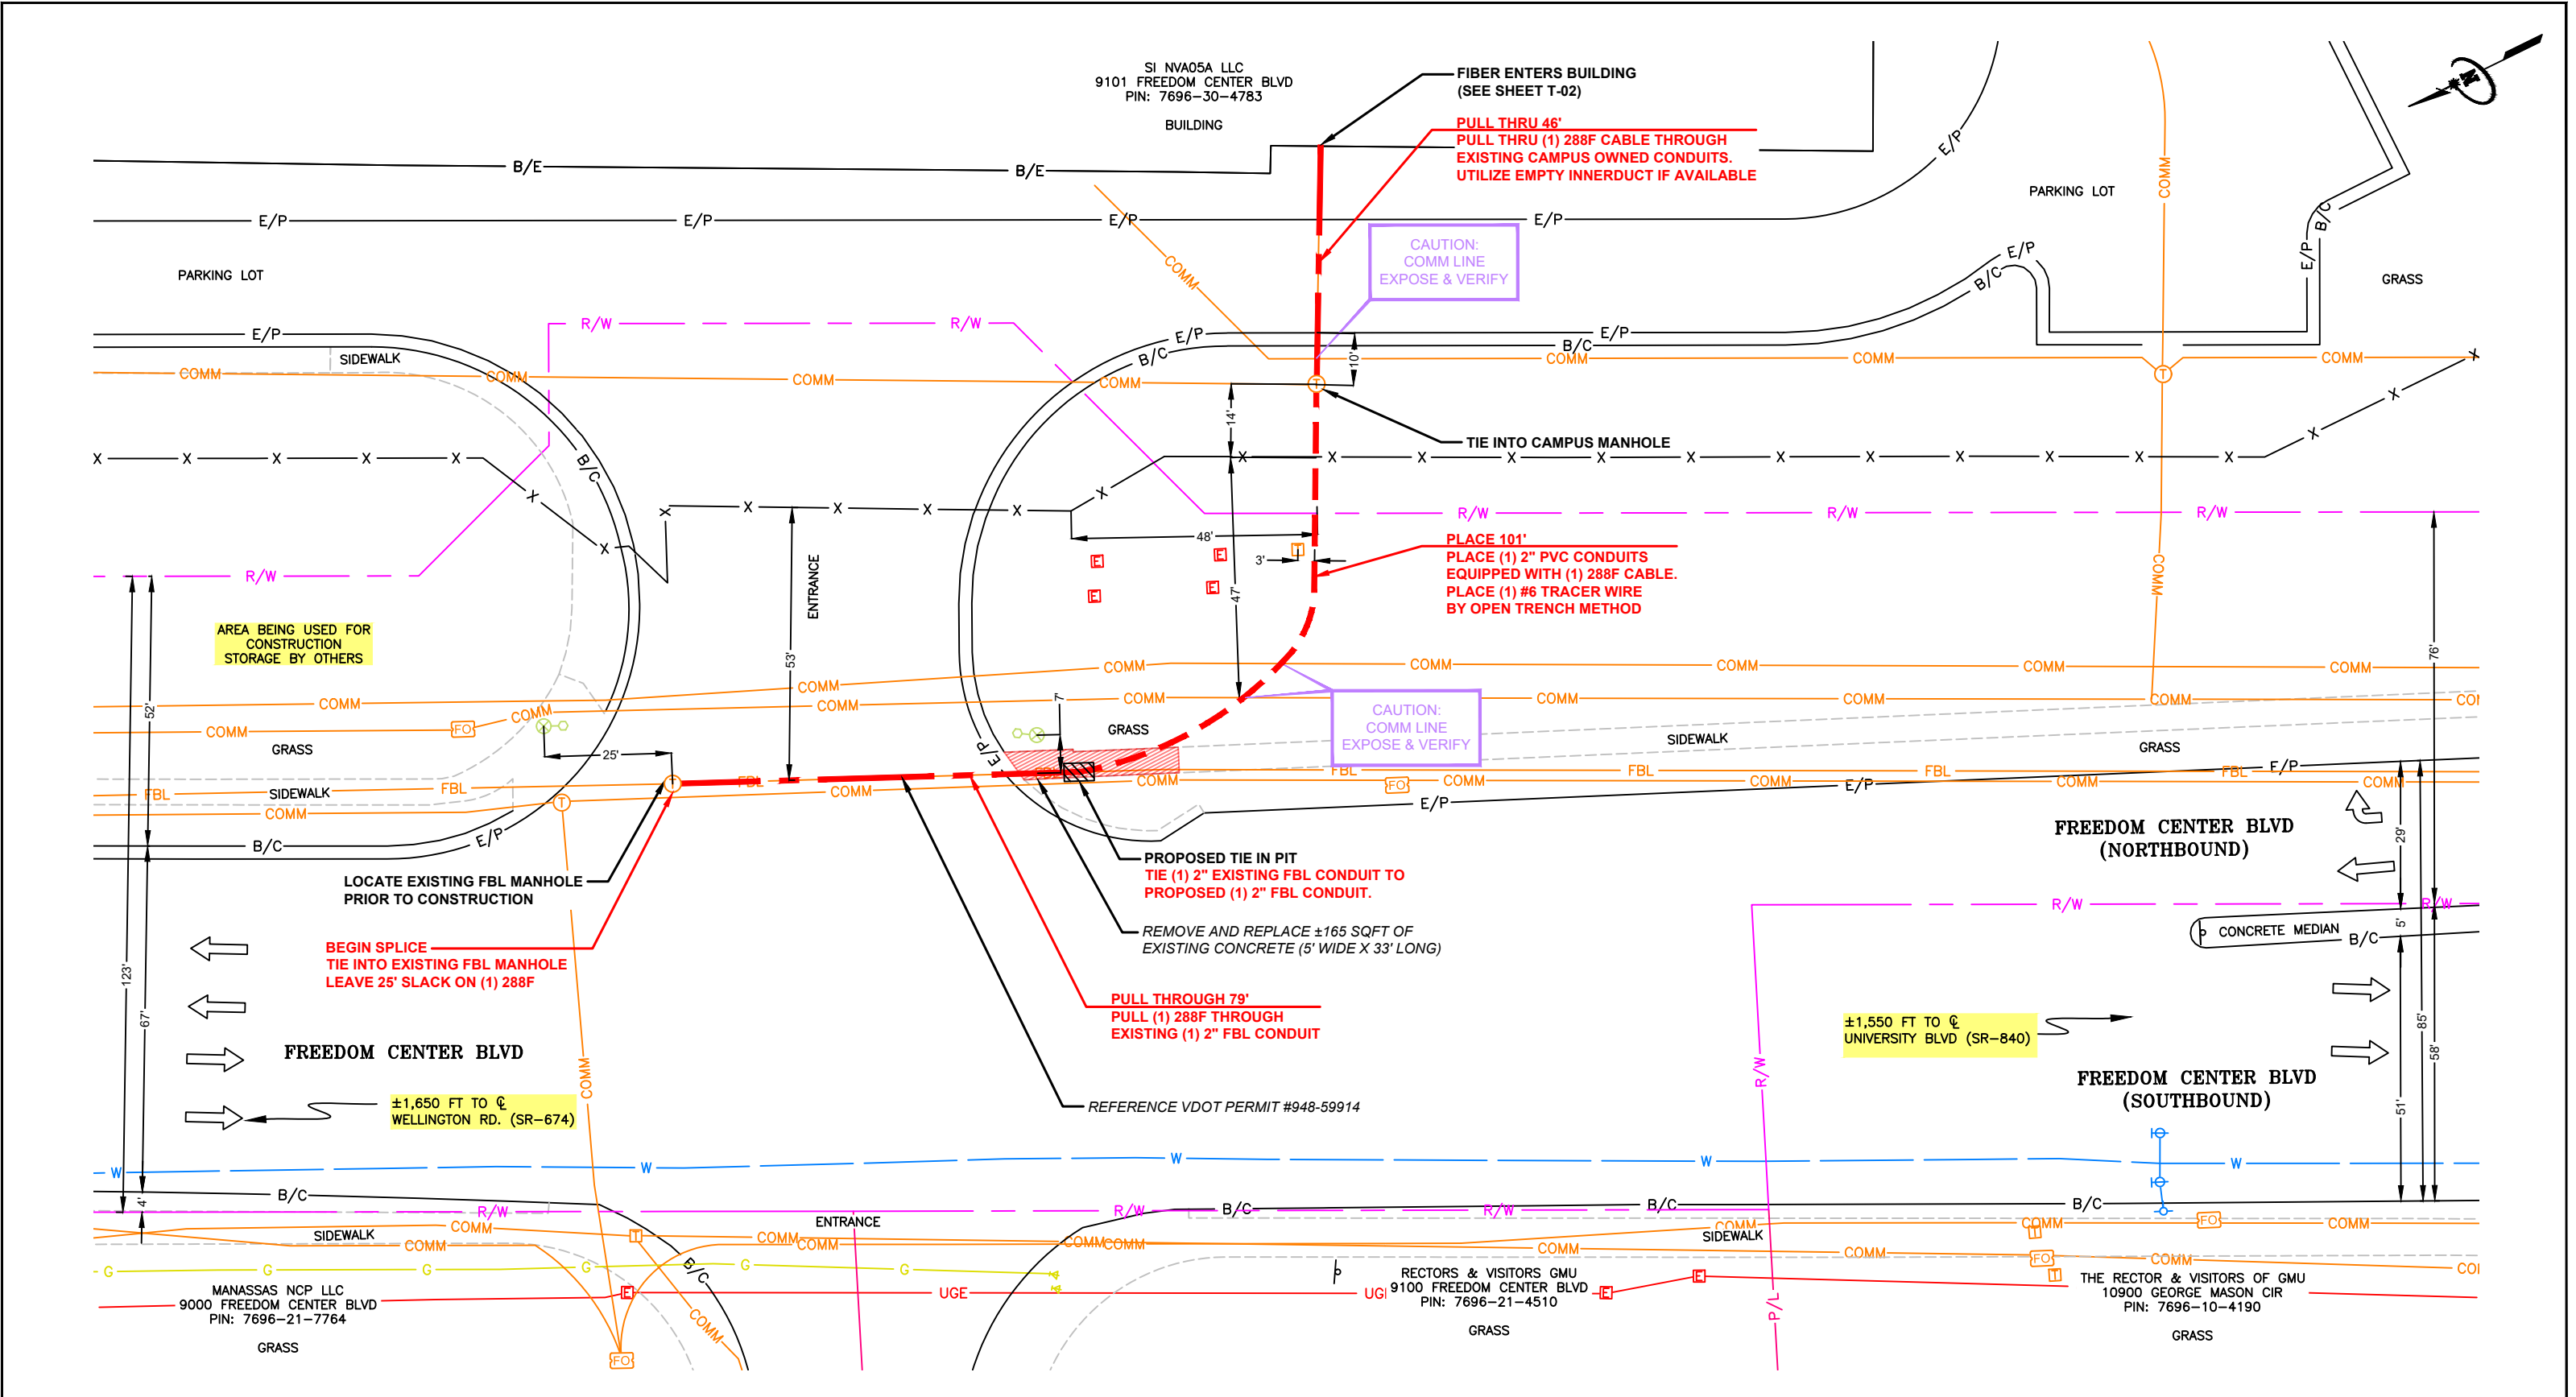

VA811.COM 1-800-552-7001		DISCLOSURE	ENGINEERING AND CONSTRUCTION FIRM	CLIENT/APPLICANT	REVISIONS			PROJECT INFORMATION					
 Call Miss Utility @ 811 before you dig.		THIS DRAWING IS ONLY A GUIDELINE AND AS SUCH DOES NOT COVER EVERY POSSIBLE CONTINGENCY THAT MAY OCCUR. INFORMATION ON THESE SHEETS HAVE BEEN PREPARED FROM THE BEST AVAILABLE INFORMATION AND SOURCES. UTILITY LOCATIONS, SIZES, AND DEPTHS ARE APPROXIMATE (UNLESS OTHERWISE NOTED) AND HAVE NOT BEEN EXCAVATED TO DETERMINE EXACT LOCATION . UTILITY/FACILITY LOCATIONS ARE BASED ON RECORDS/VERBAL INFORMATION AND PHYSICAL FEATURES AT THE TIME OF THE SURVEY. INFORMATION ON THIS DOCUMENT IS PROPRIETARY AND SHALL NOT BE USED, COPIED, REPRODUCED, OR DISCLOSED IN WHOLE OR IN PART WITHOUT WRITTEN CONSENT.	 8093 Elm Drive Mechanicsville, Virginia 23111 PHONE: 804-321-8900 FAX: 804-442-2146	 45472 HOLIDAY DRIVE, SUITE 10 STERLING, VIRGINIA 20166 PHONE: 678-366-0027 FAX: 571-323-7655	REV	DATE	DESCRIPTION	BY	FISHEL PROJECT NUMBER: 052410328	DRAWN BY: CDL	CHECKED BY: JMH		
					01	09/26/24	TIE-IN UPDATE	JMH	DRAWING TITLE: 9101 FREEDOM CENTER BLVD	DRAWING TYPE: CONSTRUCTION			
					02	10/18/24	APPROVED PERMIT	JMH	DATE: 12/24/2024	SCALE: 1:30			
					03	12/24/24	INSTALLATION METHOD UPDATE	JMH	PAGE INFORMATION				
									PLAN VIEW				
										T-01			
										SHEET 6 OF 7			

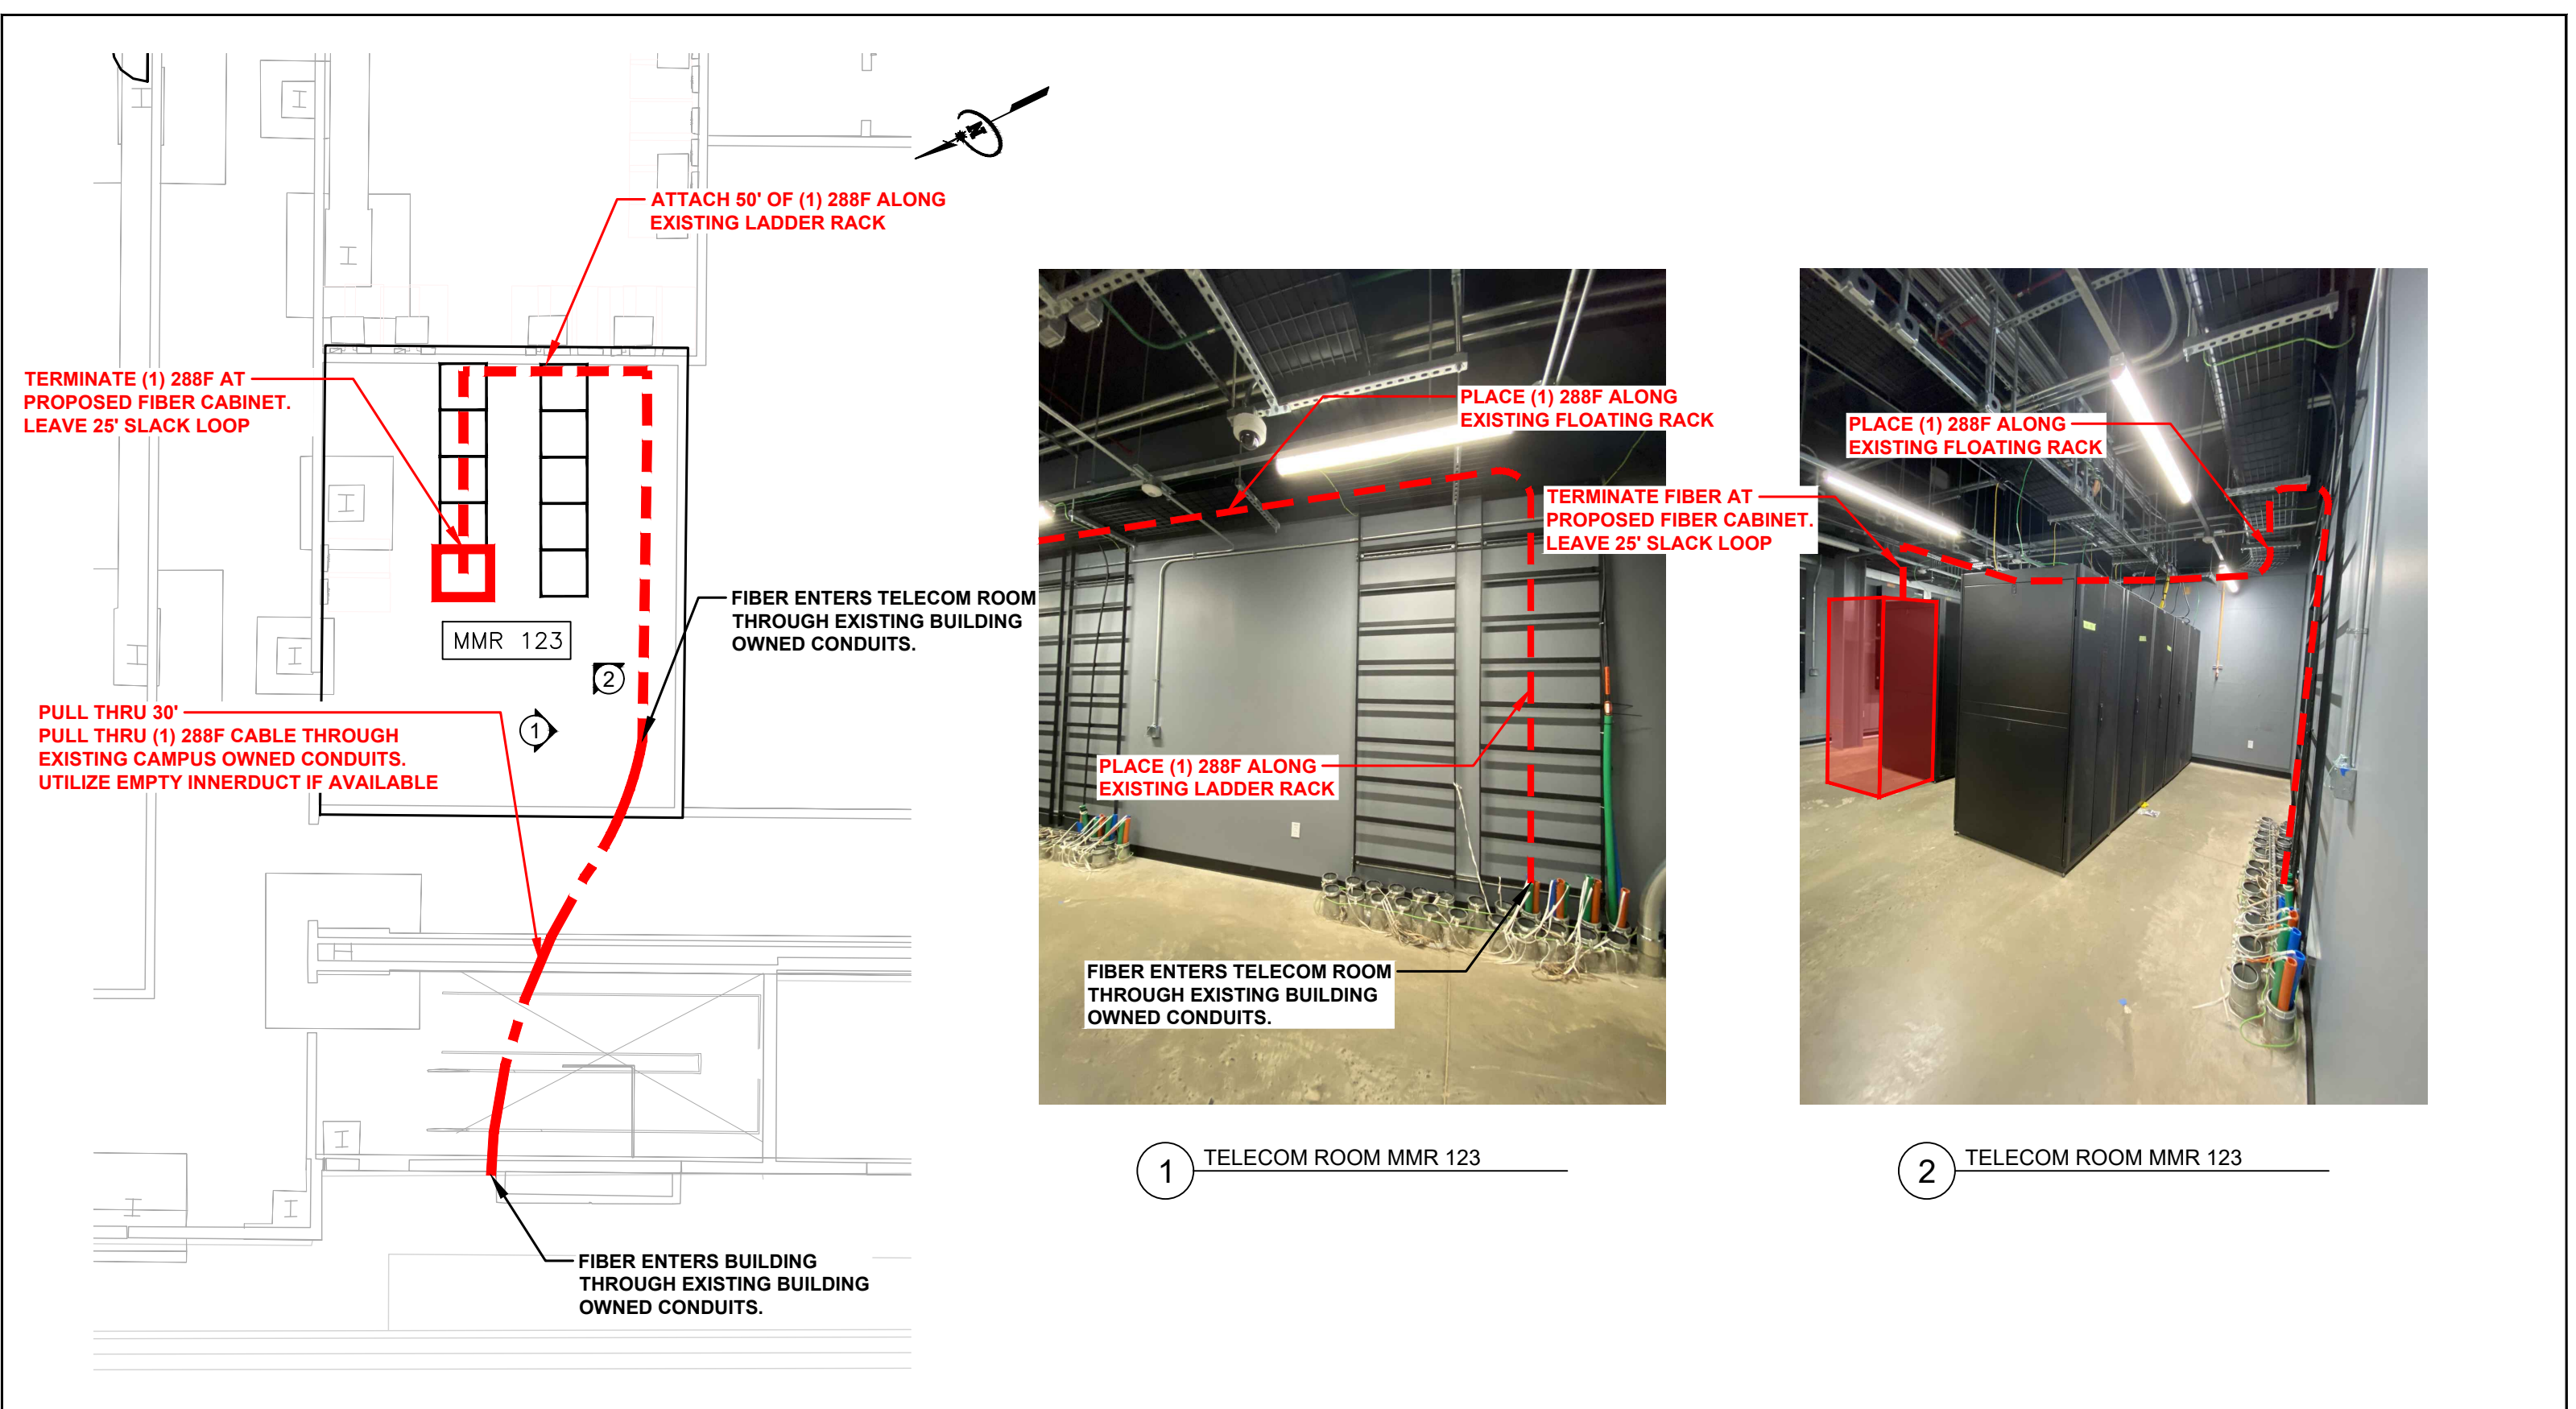

VA811.COM 1-800-552-7001		DISCLOSURE	ENGINEERING AND CONSTRUCTION FIRM	CLIENT/APPLICANT	REVISIONS				PROJECT INFORMATION			
 Call Miss Utility @ 811 before you dig.		THIS DRAWING IS ONLY A GUIDELINE AND AS SUCH DOES NOT COVER EVERY POSSIBLE CONTINGENCY THAT MAY OCCUR. INFORMATION ON THESE SHEETS HAVE BEEN PREPARED FROM THE BEST AVAILABLE INFORMATION AND SOURCES. UTILITY LOCATIONS, SIZES, AND DEPTHS ARE APPROXIMATE (UNLESS OTHERWISE NOTED) AND HAVE NOT BEEN EXCAVATED TO DETERMINE EXACT LOCATION . UTILITY/FACILITY LOCATIONS ARE BASED ON RECORDS/VERBAL INFORMATION AND PHYSICAL FEATURES AT THE TIME OF THE SURVEY. INFORMATION ON THIS DOCUMENT IS PROPRIETARY AND SHALL NOT BE USED, COPIED, REPRODUCED, OR DISCLOSED IN WHOLE OR IN PART WITHOUT WRITTEN CONSENT.	 8093 Elm Drive Mechanicsville, Virginia 23111 PHONE: 804-321-8900 FAX: 804-442-2146	 45472 HOLIDAY DRIVE, SUITE 10 STERLING, VIRGINIA 20166 PHONE: 678-366-0027 FAX: 571-323-7655	REV	DATE	DESCRIPTION	BY	FISHEL PROJECT NUMBER: 052410328	DRAWN BY: CDL	CHECKED BY: JMH	
					01	09/26/24	TIE-IN UPDATE	JMH	DRAWING TITLE: 9101 FREEDOM CENTER BLVD	DRAWING TYPE: CONSTRUCTION		
					02	10/18/24	APPROVED PERMIT	JMH	DATE: 12/24/2024	SCALE: NTS		
					03	12/24/24	INSTALLATION METHOD UPDATE	JMH	PAGE INFORMATION			
									PLAN VIEW			T-02
										SHEET 7 OF 7		