




-  **Diesel Fuel**
Exterior USTs
-  **Nitrogen**
Fire Pump Room
-  **Potassium Hydroxide**
Generator Paralleling
Room A and B

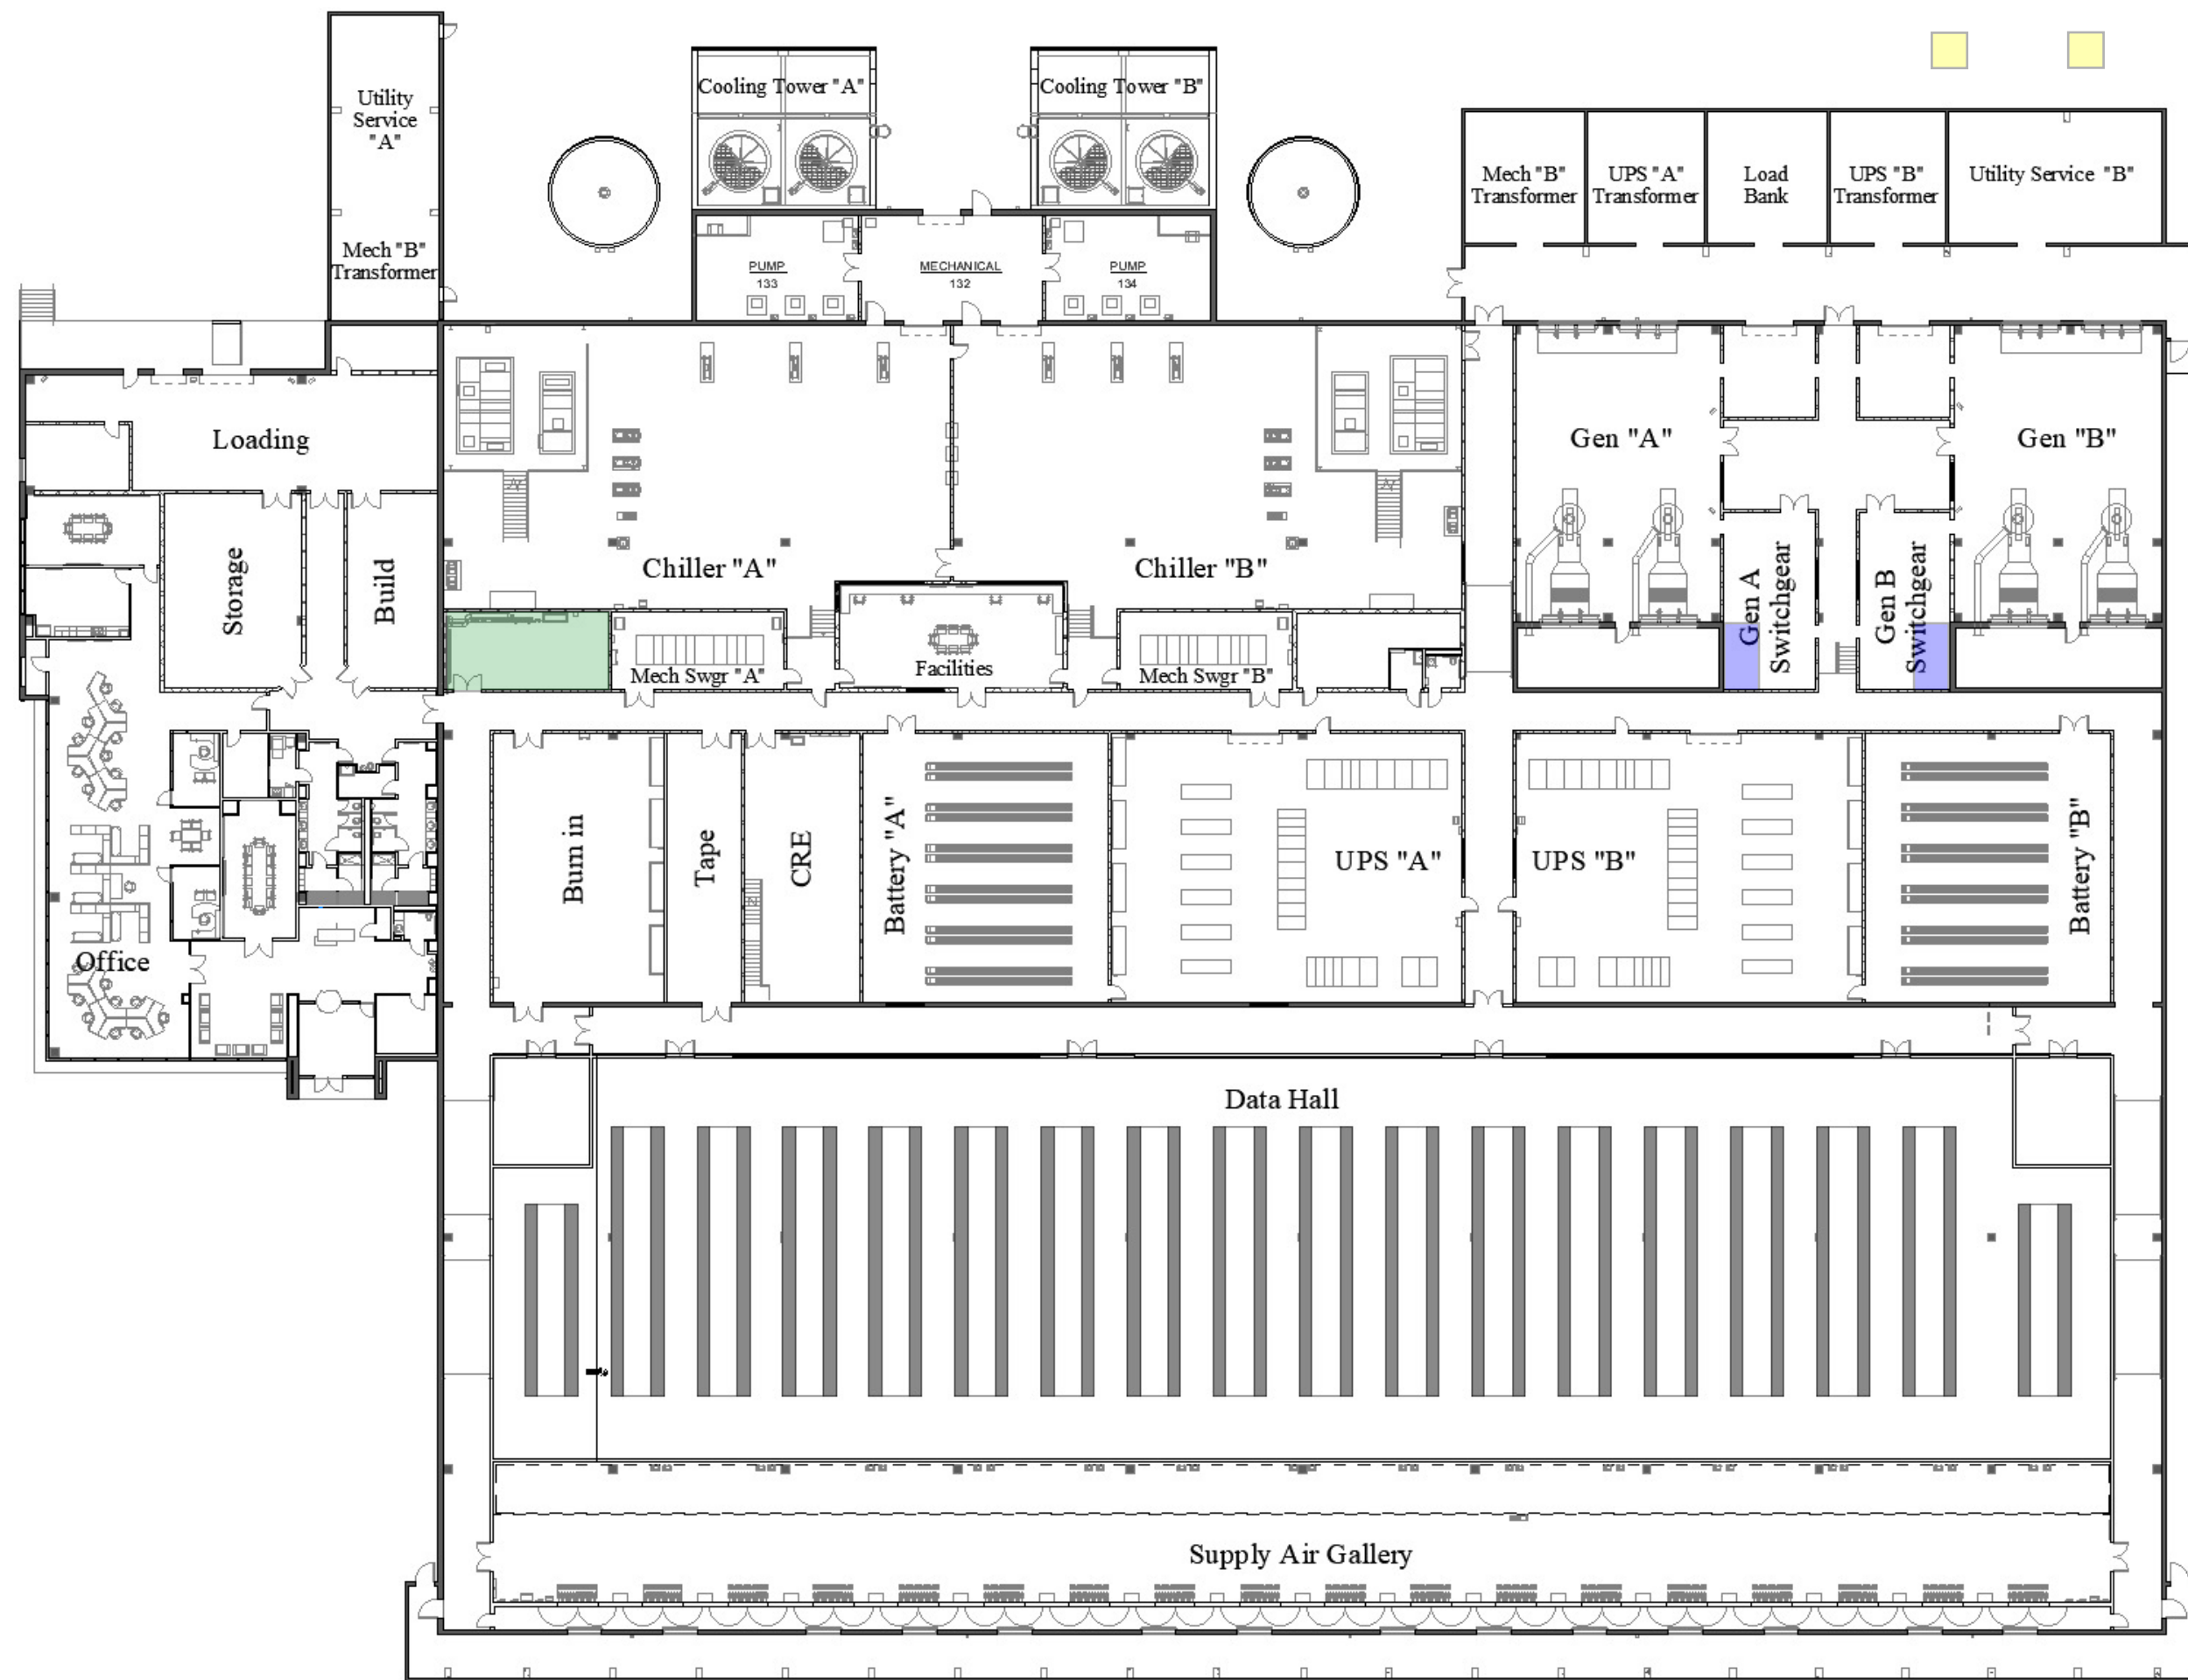

STACK NAL01A FLOOR PLAN

7300 SOUDER RD
NEW ALBANY, OH 43054
MARCH 24, 2020