



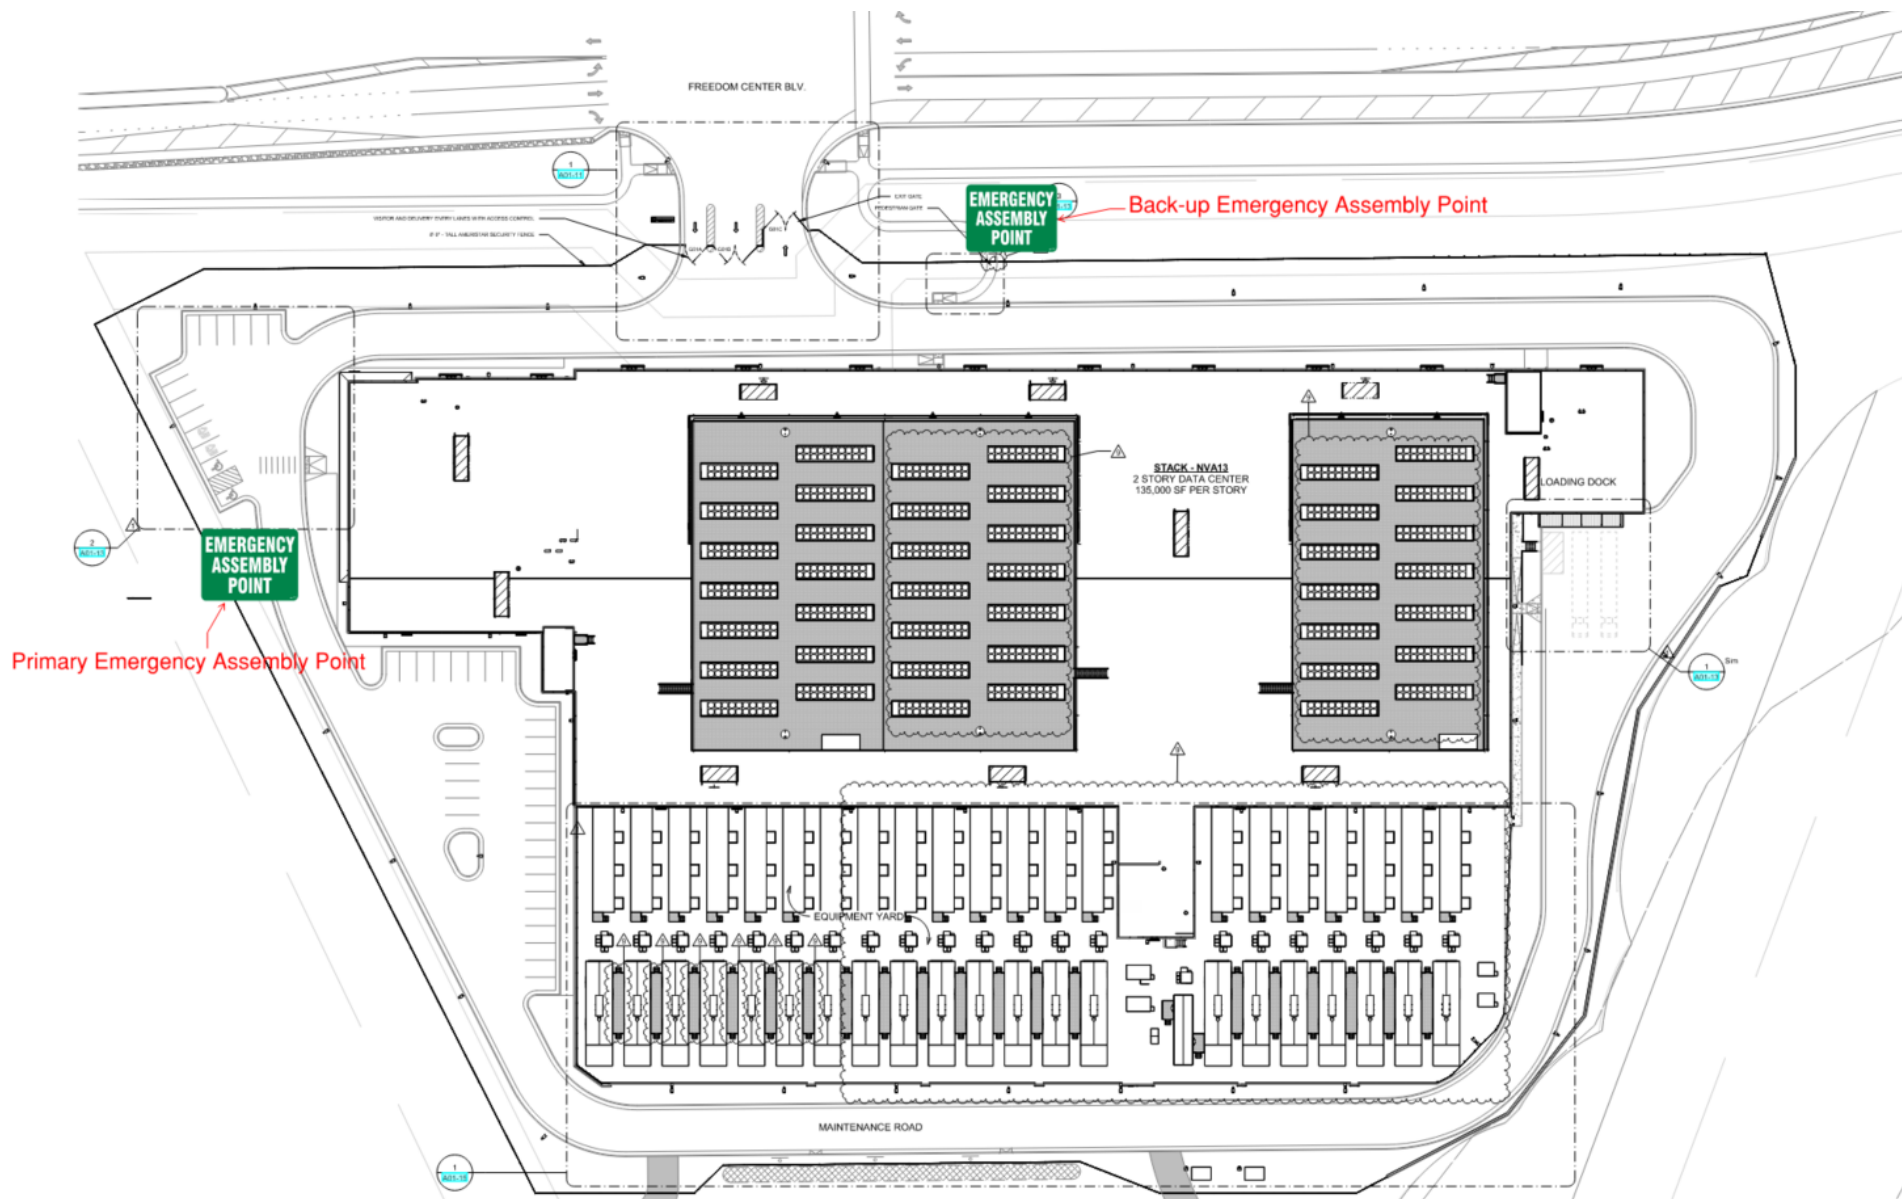


EXTERIOR

EMERGENCY EVACUATION PLAN

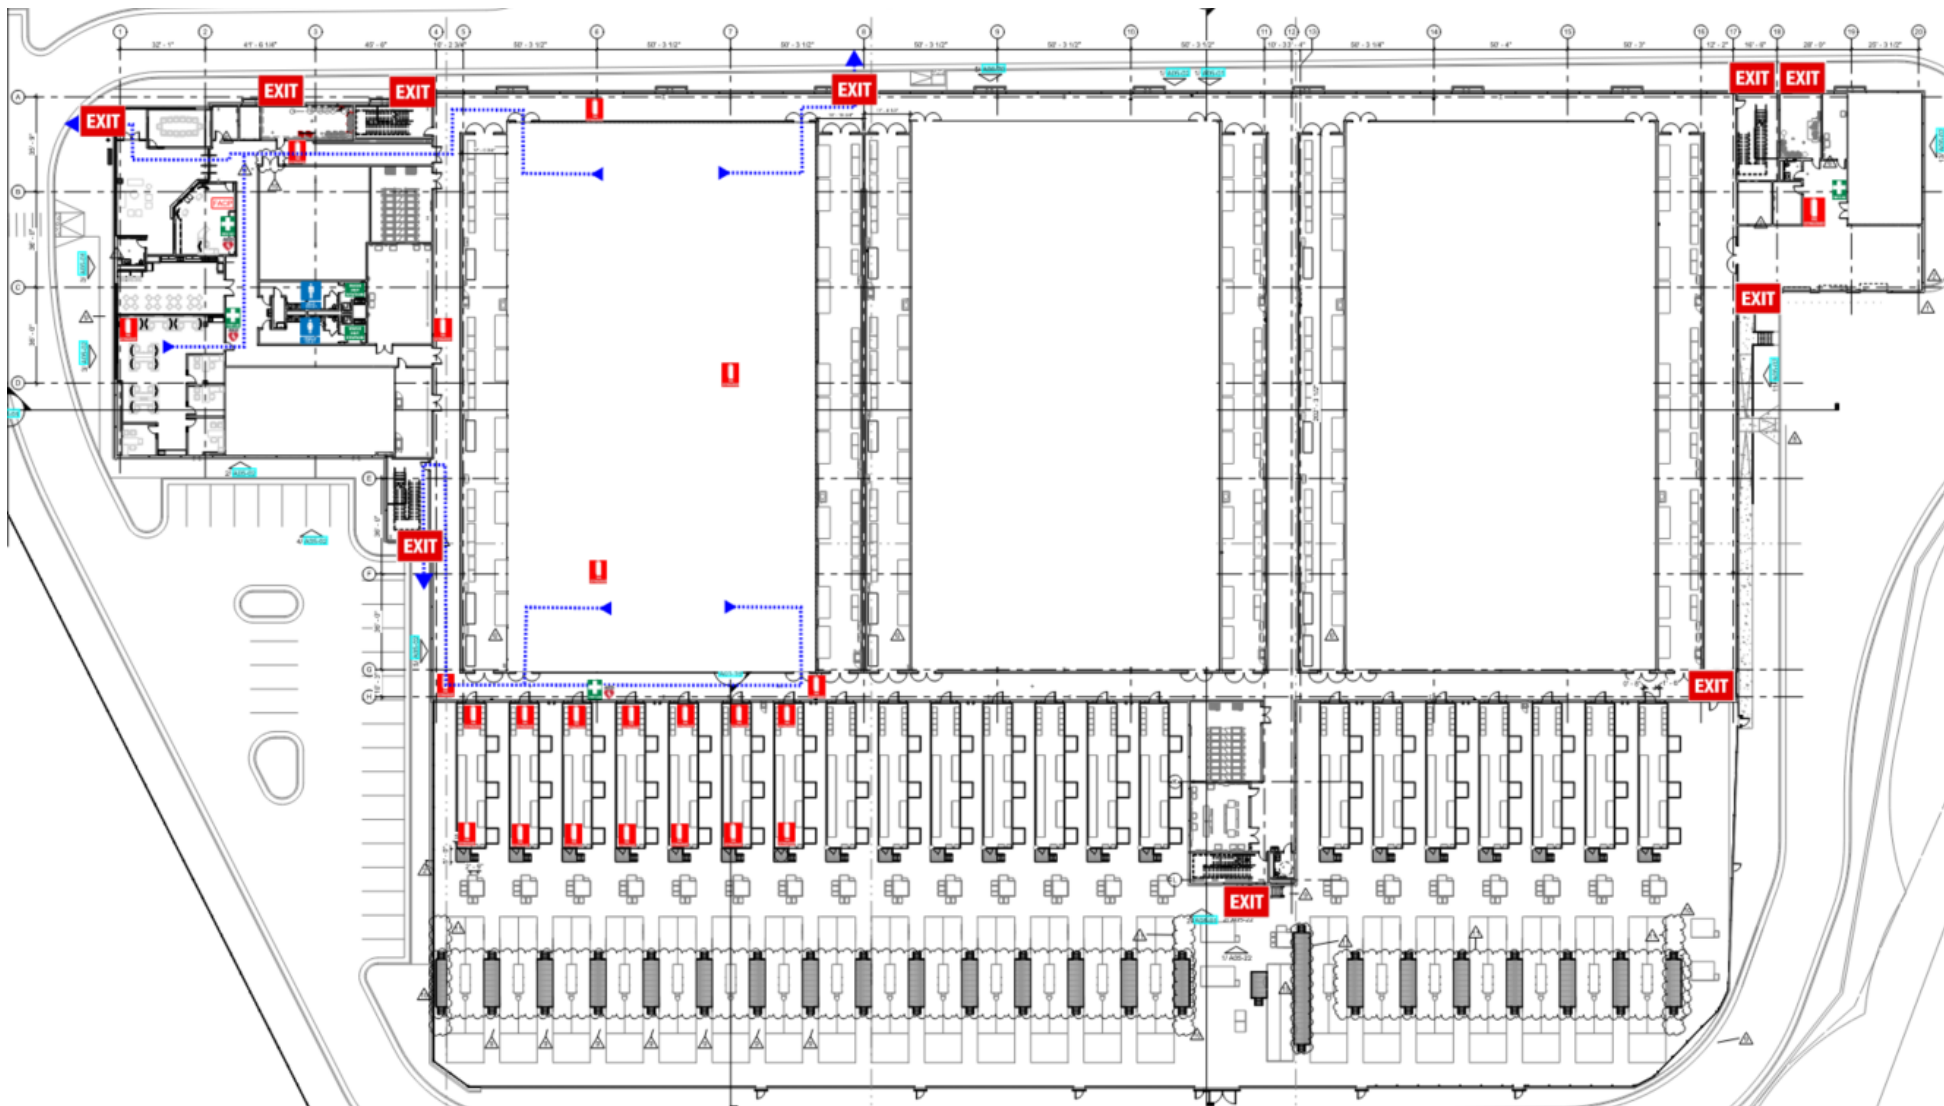

FIRST FLOOR

EMERGENCY EVACUATION PLAN

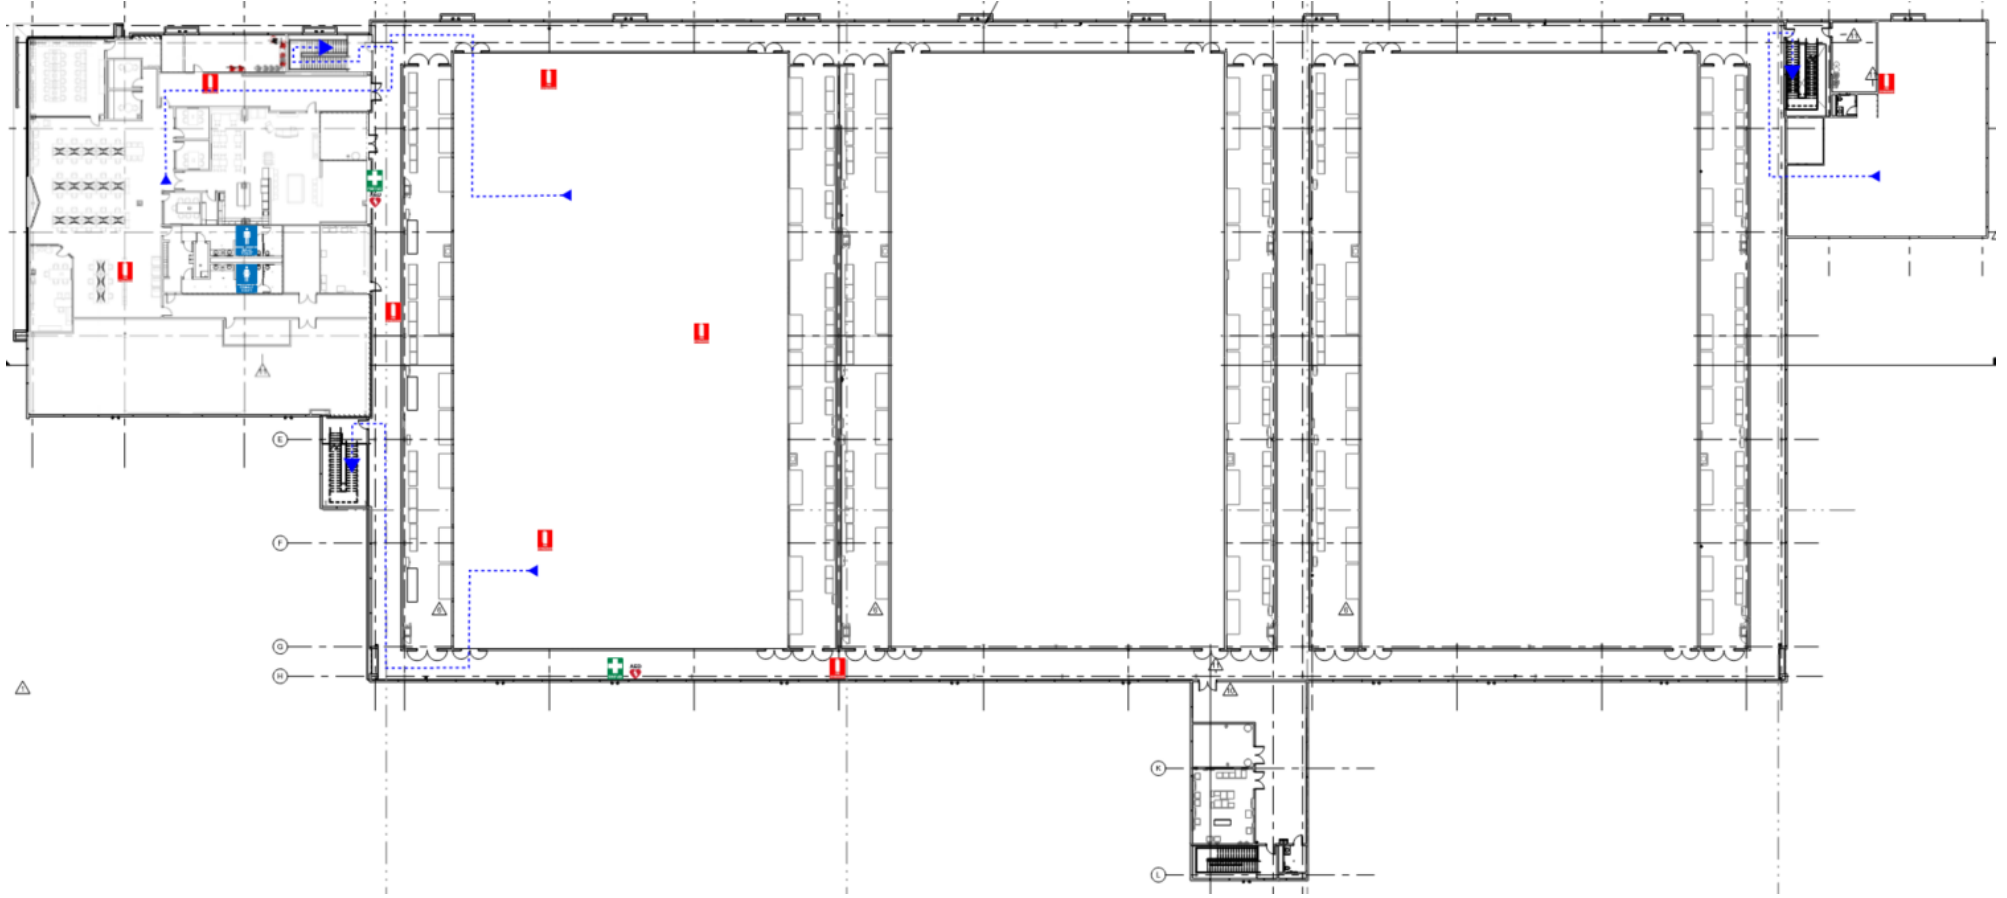

SECOND FLOOR

EMERGENCY EVACUATION PLAN